会签	给水 排水		建筑 结构		电气 仪表		设备 暖通		道路 桥梁		水工 环境		景观 总体	

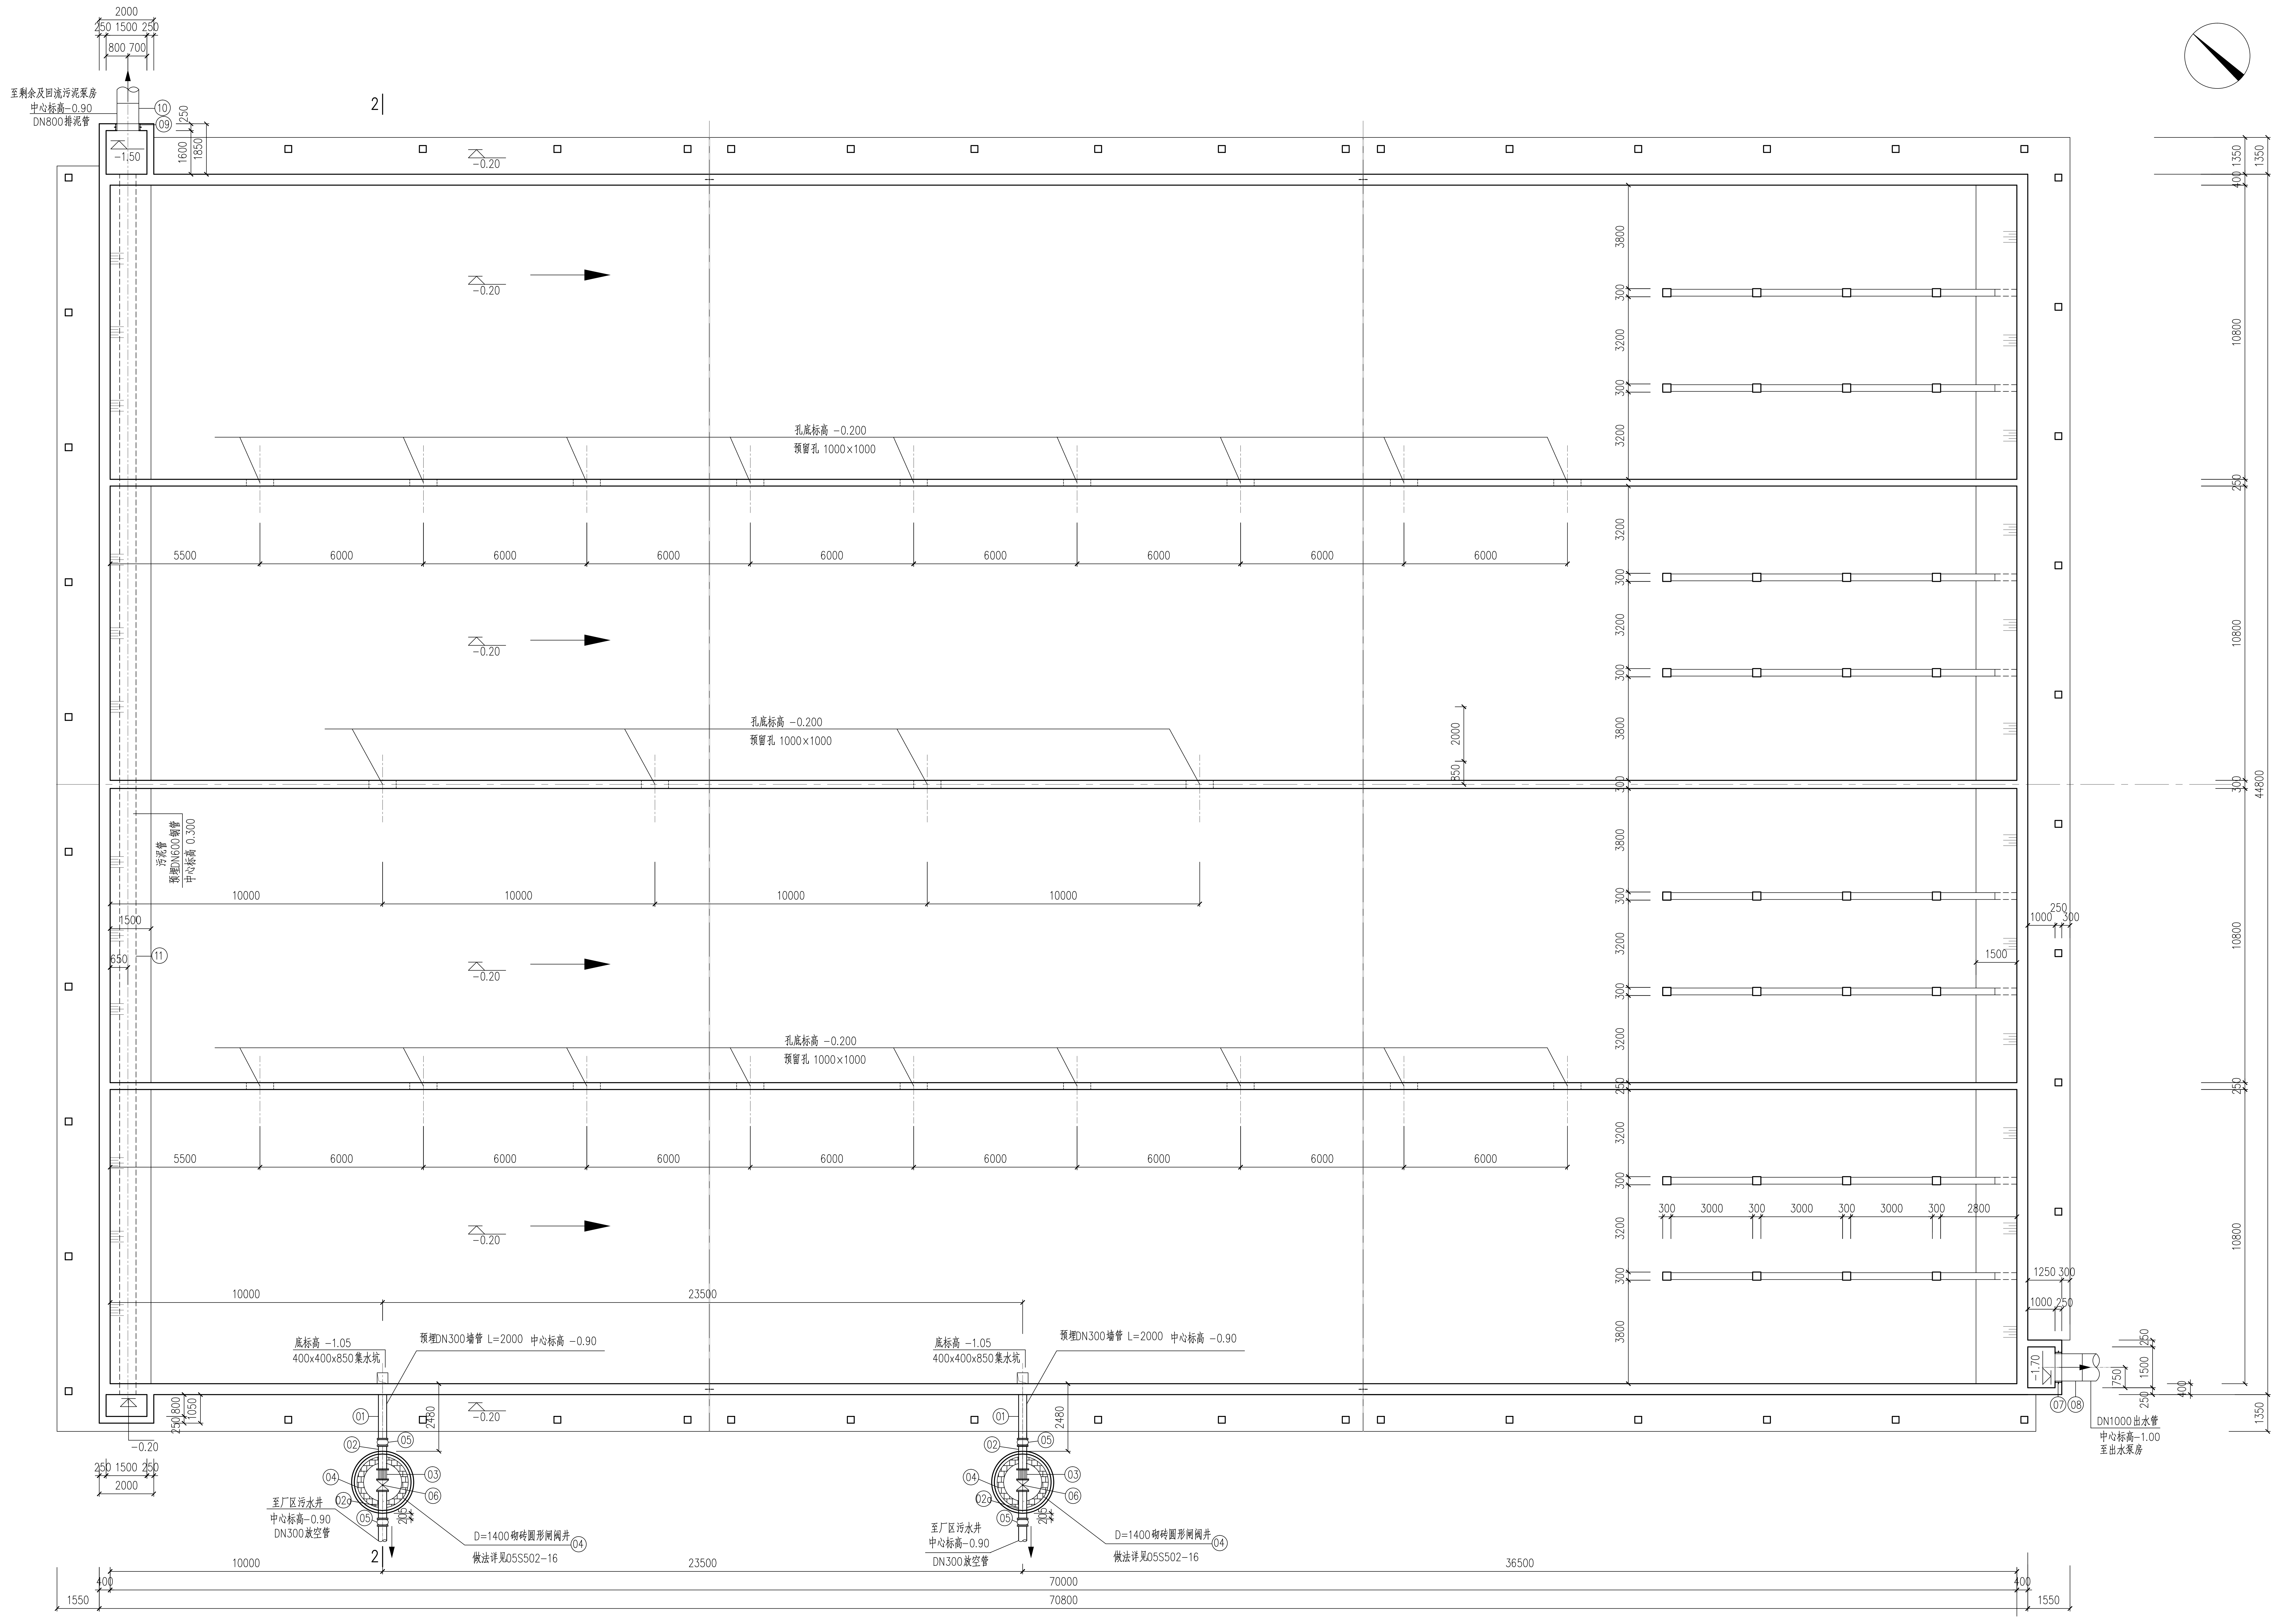

下层平面图 1:100

			校　核 CHECKED	蒋丽君		阶　段 STAGE	施工图设计	上海市政工程设计研究总院(集团)有限公司 SHANGHAI MUNICIPAL ENGINEERING DESIGN INSTITUTE (GROUP) CO., LTD. SMEDI	奉贤西部污水厂升级改造及三期扩建工程	项目编号 PROJECT NO.	2014SH405SS
审　核 AGREED	胡维杰		校　对 CHECKED	蒋丽君		专　业 SPECIALITY	排水			子项名称 SUB ITEM	三期二沉池
设计负责人 CHIEF DESIGNER	蒋丽君		设　计 DESIGNED	朱佳斌		比　例 SCALE	1:100		三期二沉池工艺设计图(一)	图　号 DRAWING NO.	DC303D-01
专业负责人 SPECIALITY SPONSOR	蒋丽君		制　图 DRAWING			日　期 DATE	2016.11.21			修正号 REV NO.	

M03000GTXF

M03000GTXF