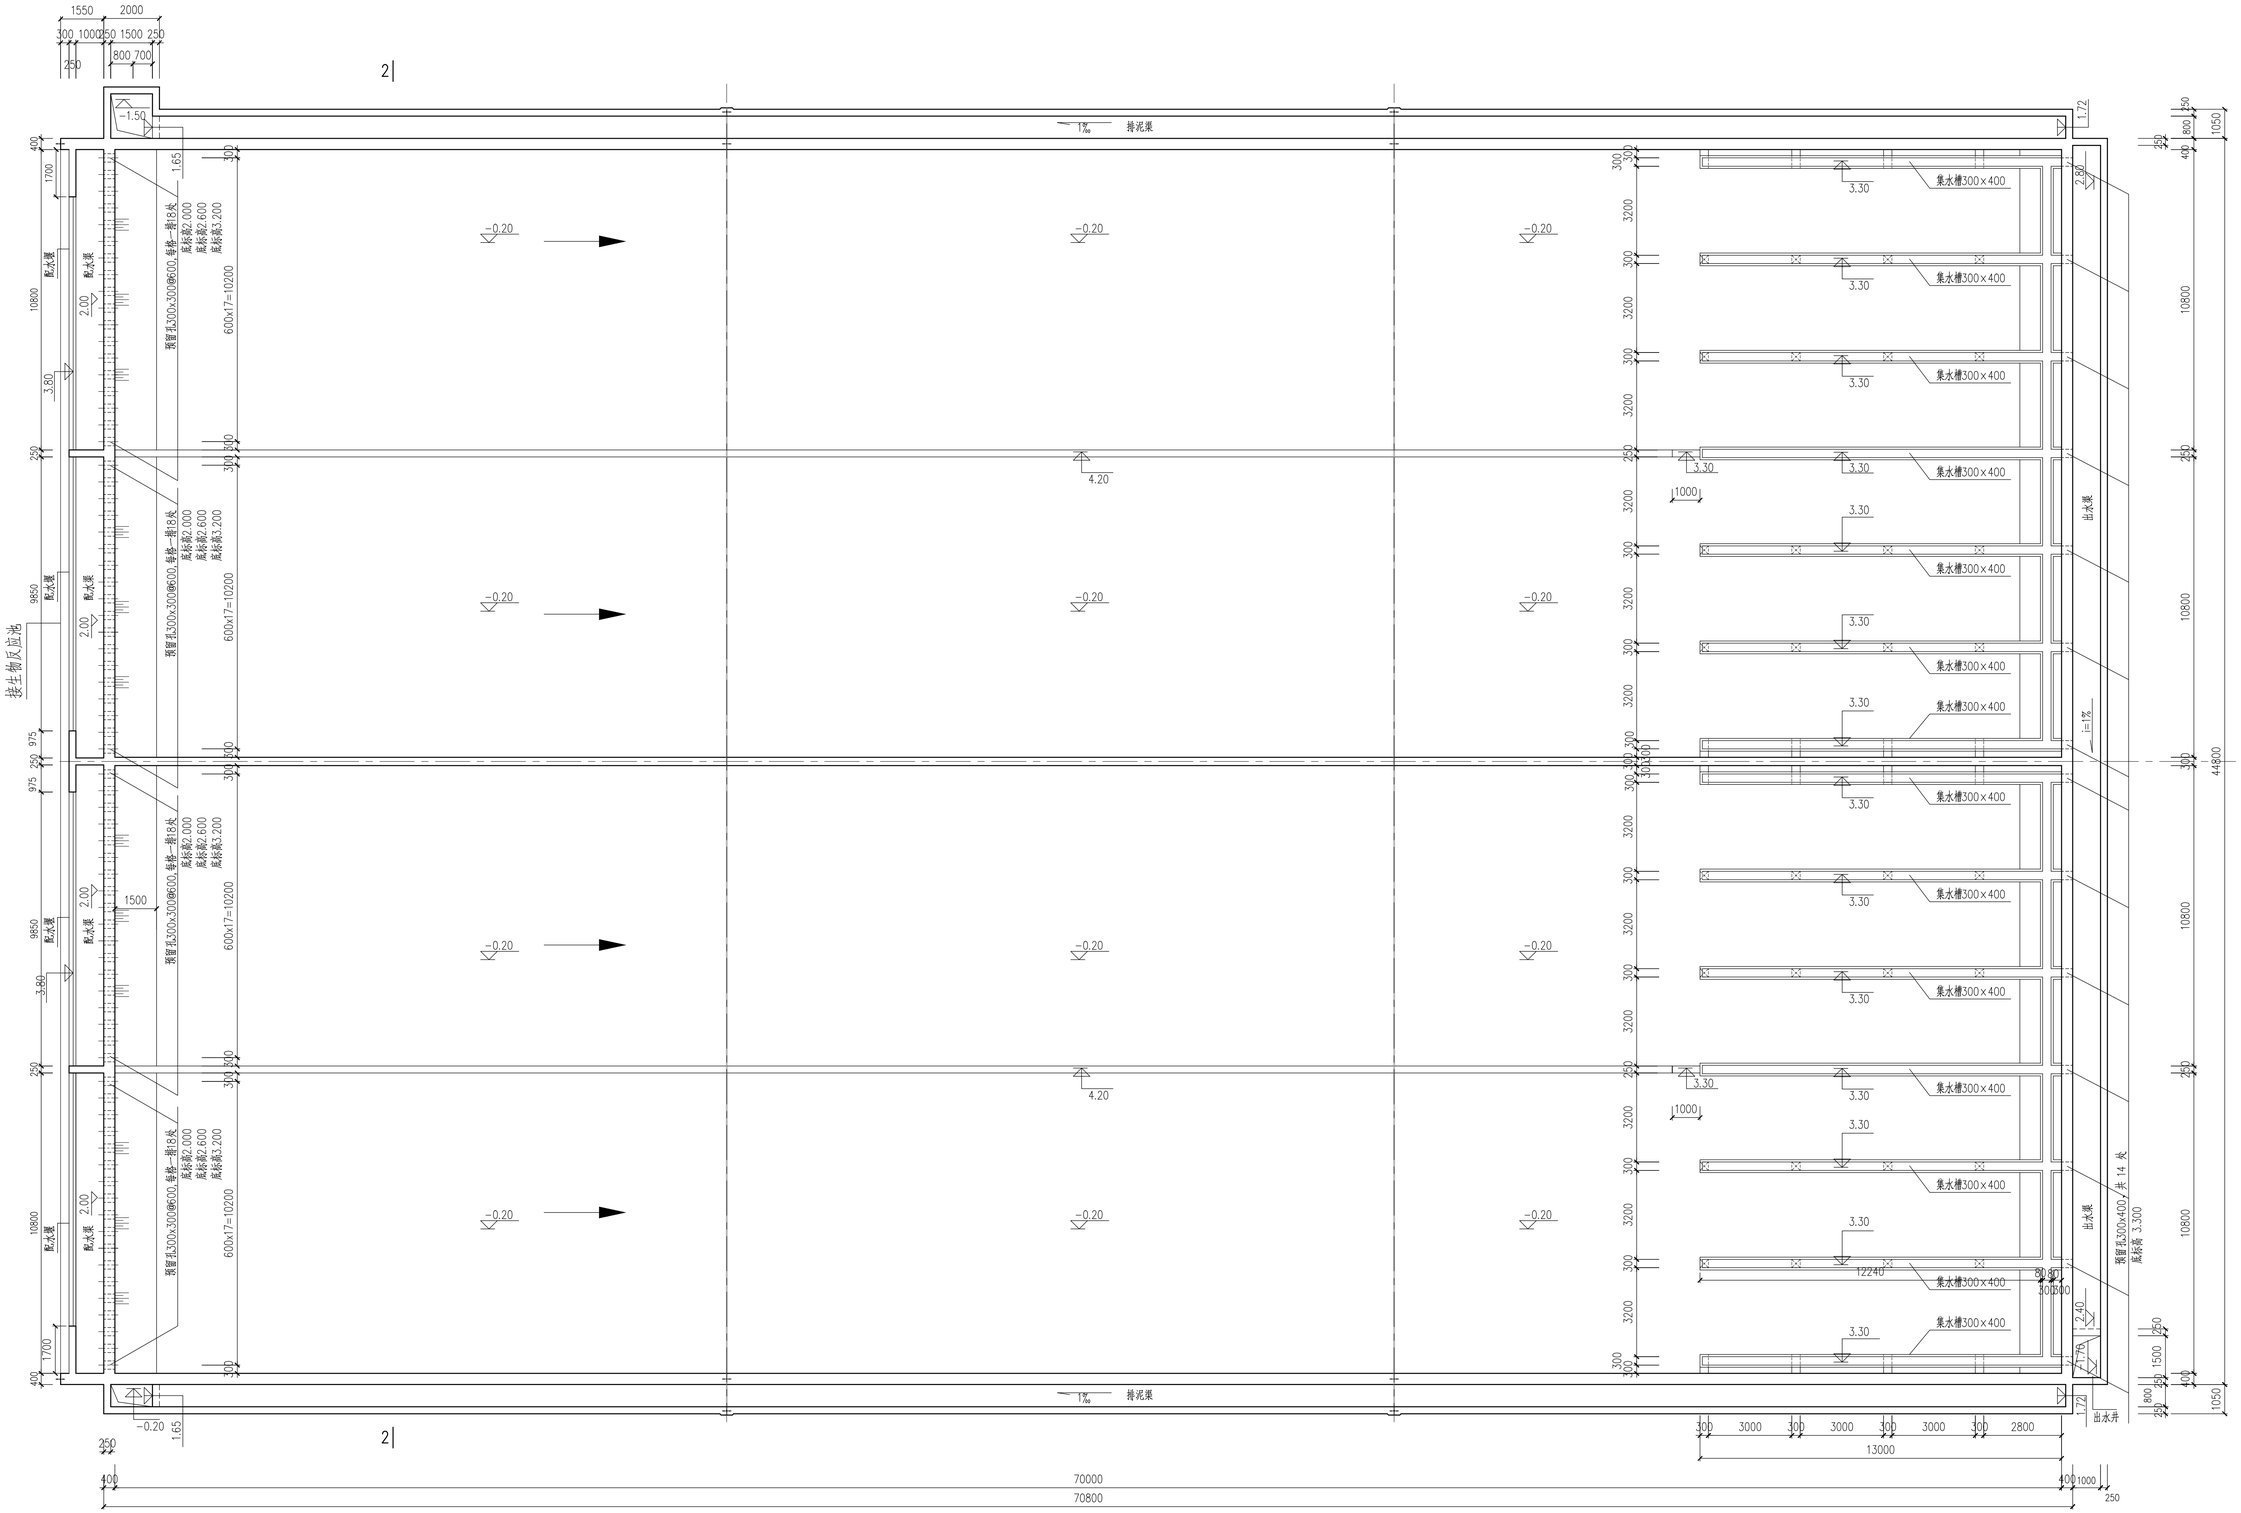


			校 核 CHECKED	蒋丽君		阶 段 STAGE	施工图设计	
审 核 AGREED	胡维杰		校 对 CHECKED	蒋丽君		专 业 SPECIALITY	排水	
设计负责人 CHIEF DESIGNER	蒋丽君		设 计 DESIGNED	朱佳斌		比 例 SCALE	1:100	
专业负责人 SPECIALITY SPONSOR	蒋丽君		制 图 DRAWING			日 期 DATE	2016.11.21	

上海市政工程设计研究总院(集团)有限公司
SHANGHAI MUNICIPAL ENGINEERING DESIGN INSTITUTE (GROUP) CO., LTD.

奉贤西部污水厂升级改造及三期扩建工程

三期二沉池工艺设计图(二)

项目编号 PROJECT NO.	2014SH405SS
子项名称 SUB ITEM	三期二沉池
图 号 DRAWING NO.	DC303D-02
修 正 号 REV. NO.	

M03000GTXG